



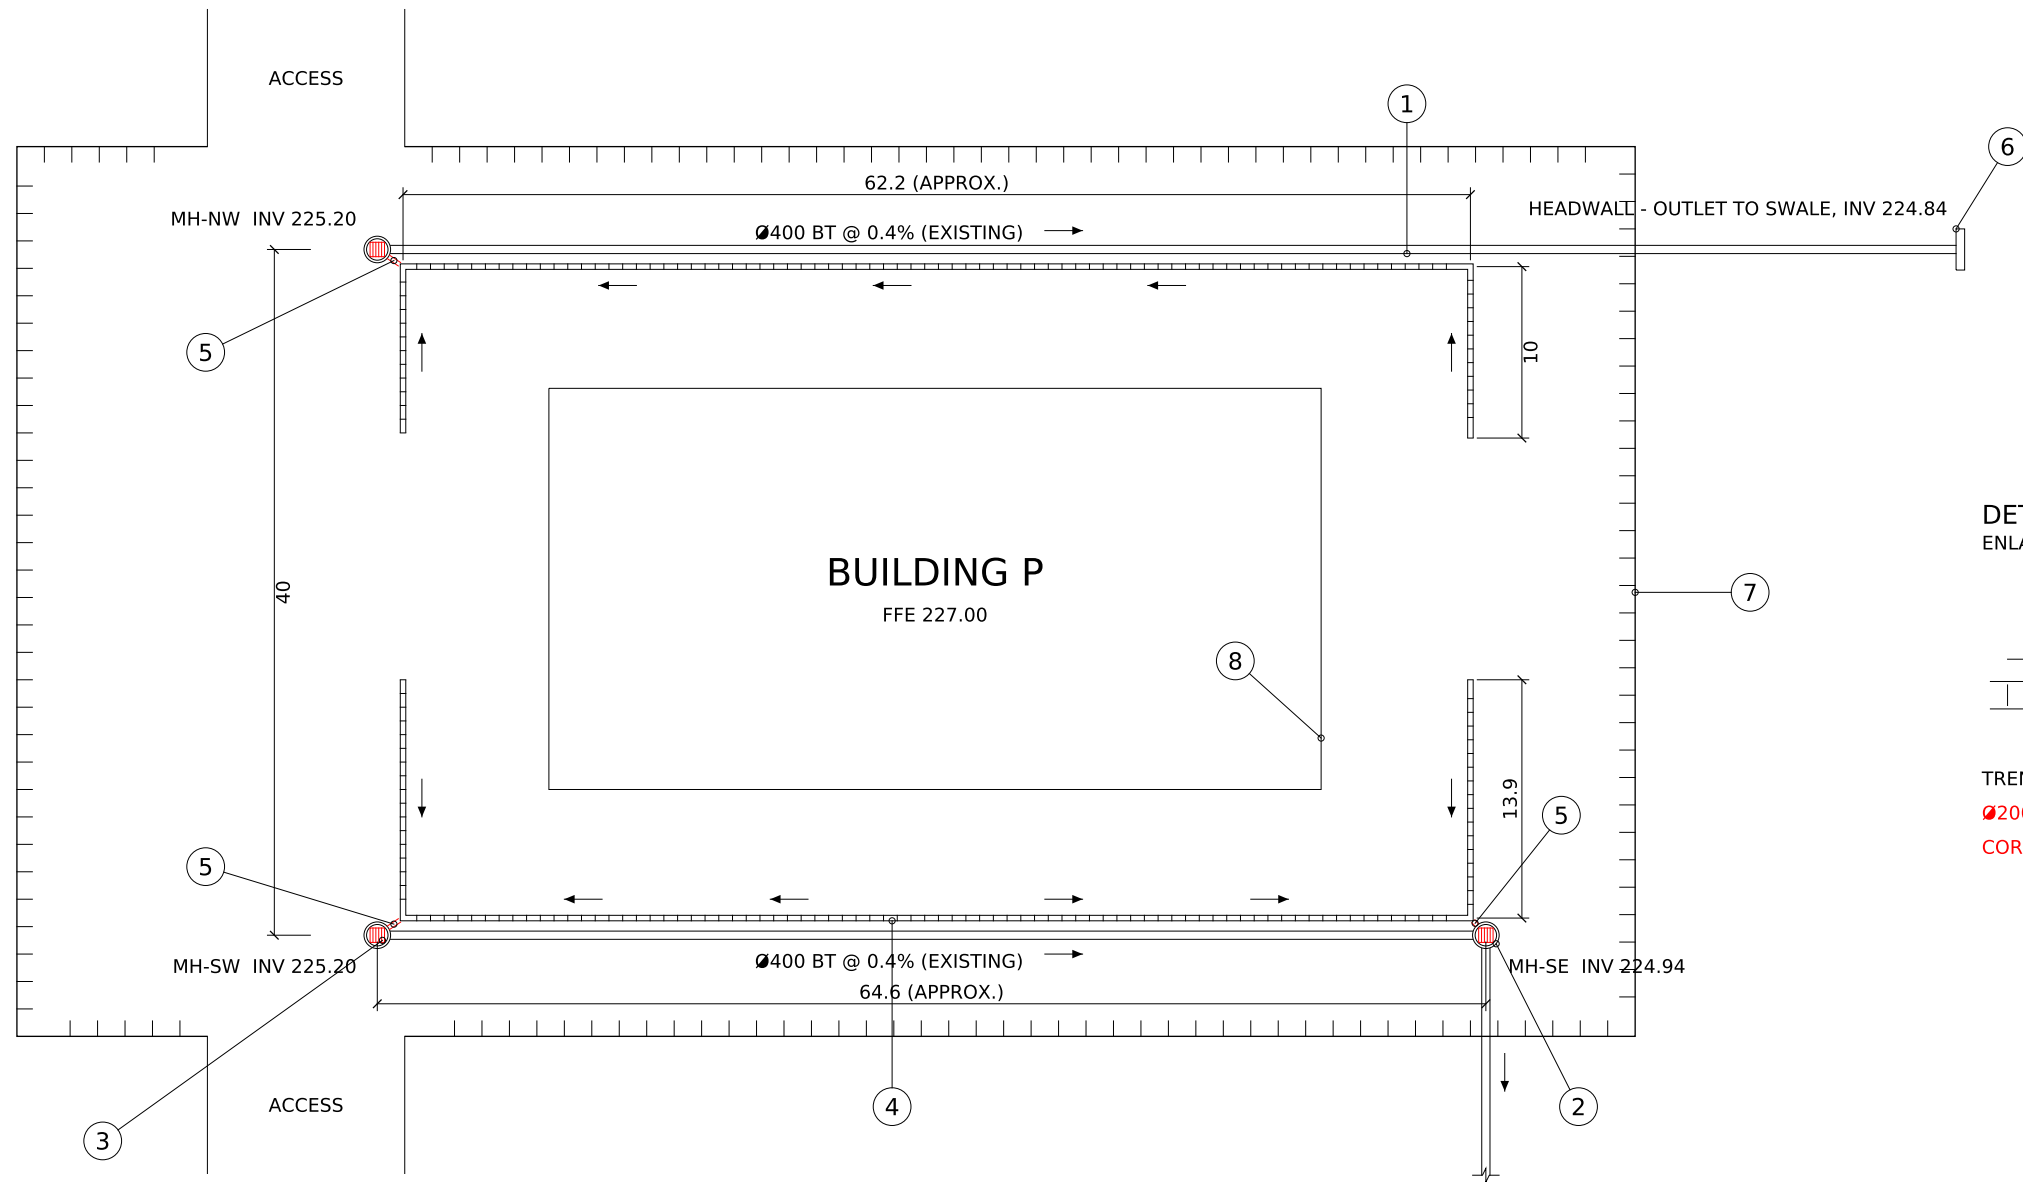

DETAIL 1 - TYPICAL CONNECTION (PLAN)
ENLARGED APPROX. 1:80

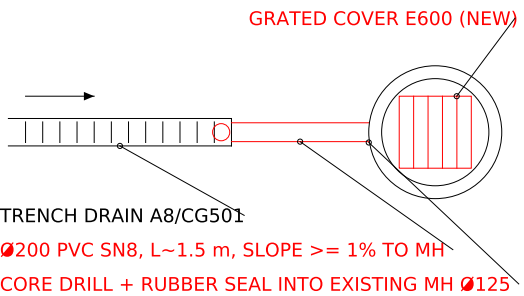

LEGEND / מקרא

No.	DESCRIPTION	תיאור
1	EXISTING Ø400 BT DRAINAGE PIPE (INSTALLED)	צינור ניקוז Ø400 בטון קיים - מותקן
2	EXISTING CONCRETE DRAINAGE MANHOLE Ø125 (INSTALLED)	שוחת ניקוז קיימת מבטון Ø125 - מותקנת
3	PROPOSED: GRATED COVER E600 INSTEAD OF CLOSED LID	מוצע: מכסה רשת E600 בשוחה במקום מכסה אטום
4	TRENCH DRAIN (PRECAST CHANNEL, A8/CG501)	תעלת ניקוז טרומית - פרט A8/CG501
5	PROPOSED: Ø200 FROM TRENCH OUTLET DIRECTLY INTO MANHOLE (INSTEAD OF INTO Ø400, E5/CG501)	מוצע: חיבור Ø200 מקצה התעלה ישירות לשוחה, במקום לצינור Ø400 לפי פרט E5
6	EXISTING CONCRETE HEADWALL - OUTLET TO SWALE	ראש קיר בטון קיים - יציאה לתעלה
7	TOE OF BERM	רגל סוללה
8	BUILDING P (FFE 227.00)	מבנה P - מפלס רצפה 227.00

- NOTES:
- PROPOSAL: TRENCH DRAINS DISCHARGE DIRECTLY INTO THE EXISTING DRAINAGE MANHOLES (MH-NW, MH-SW, MH-SE). THE Ø200 DISCHARGE INTO THE Ø400 BT PIPE PER E5/CG501 IS CANCELLED.
 - MANHOLE COVERS: GRATED COVER CLASS E600 (EN 124) INSTEAD OF CLOSED LID.
 - CONNECTION INTO MANHOLE WALL BY CORE DRILLING + RUBBER SEAL. MANHOLE BENCHING PER GOVT REMARK 57 00 00-7.2 (b).
 - Ø200 INVERTS AND TRENCH DRAIN SLOPES PER COORDINATED PROFILE (GOVT REMARK c.i) - TO BE ISSUED.
 - RED = PROPOSED. DIMENSIONS IN METERS, SCALED FROM CG104/CG105 - APPROXIMATE.

BUILDING P - TRENCH DRAIN CONNECTION TO EXISTING MANHOLES - PROPOSAL (PLAN VIEW)
HATZERIM 20117 | REF: CG104, CG105, CG501 (A8, C8, E5), TRANSMITTAL 57 00 00-7.2 | SCALE 1:400 (A3)